

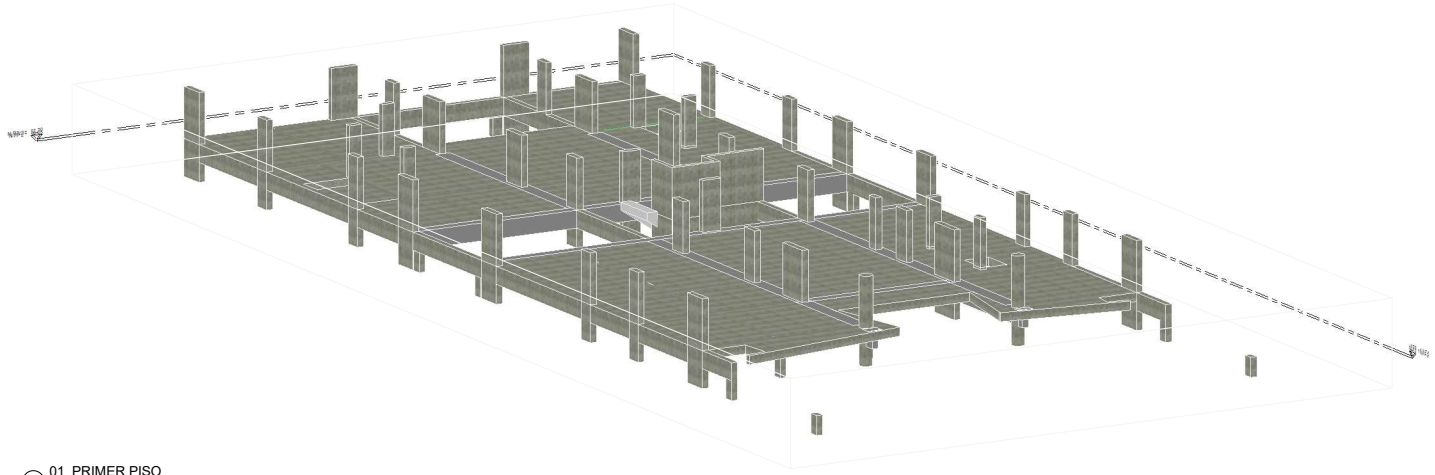



1 01_PRIMER PISO

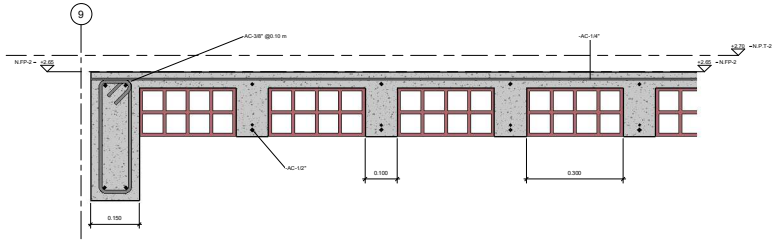


3 SECCION ALIGERADO TIPICO
1 : 5

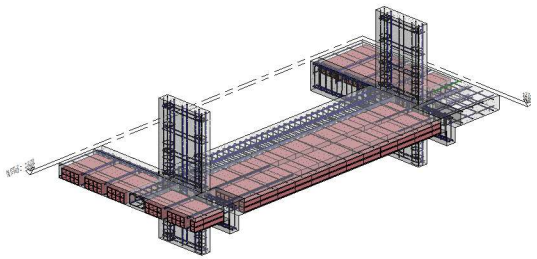


2 DETALLE ACERO DE VIGA-COLUMNA

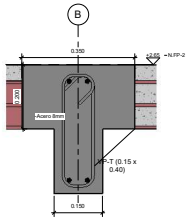

6 VP-T (0.15 X 0.35)
1 : 5

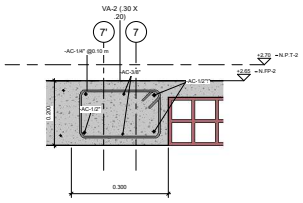

4 VA-2 (0.30 X 0.20)
1 : 5

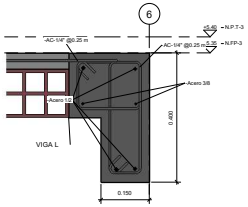

5 VA-3 (0.15 X 0.40)
1 : 5

GRUPO 5
CONSULTORA EN MODELADOS ESTRUCTURALES
EDIFICIOS MULTIFAMILIARES

Proyectista:
FLORENCIO ISIFRO GAMBOA

Contratista:
CARLOS HINOSTROZA BURBANO

Cliente:
Universidad Nacional de Ingeniería

Supervisión:	Firma:
INGENIEROS	

APROBADO SIN COMENTARIOS	Cód. 1	
APROBADO CON COMENTARIOS	Cód. 2	
REVISAR Y REENVIAR	Cód. 3	

RESPONSABLES MODELADORES

ZAPATAS	--TORRES ROJAS, Jairo Kevin
COLUMNAS	--Espinal Cerron Paul Jhobby
CONCRETO SIMPLE	--Ccana Ayuque Joseph Leonardo
VIGAS DE CONEXION	--Ramos Borjas José Miguel

Proyecto:
VIVIENDA MULTIFAMILIAR

Ubicación:
CALLE FELIZ SAMANIEGO
MZ X LOTE 4
URBANIZACION COVIMA

Distrito:
LA MOLINA

Escala:
1 : 5

Lámina:
02