
ESPACIO	AFORO
TALLER DE CONFESIÓN DE CALZADO Y ROPA	12
TALLER DE SERVICIOS EXISTENCIALES	12
TALLER DE ESTETICA PROFESIONAL	12
TALLER DE HOSTELERIA Y TURISMO	14
TALLER DE COCINA Y REPOSTERIA	15
TALLER INDUSTRIA DEL VESTIDO	27
TALLER DE ELECTRICIDAD	20
TALLER DE COMPUTACION	12
LABORATORIO DE COMPUTO	22
AUDITORIO	200
SALA DE PROYECCION	16
OFICINA DE LA DIRECCIÓN	4
OFICINA ADMINISTRATIVA	5
CAFETERÍA	32

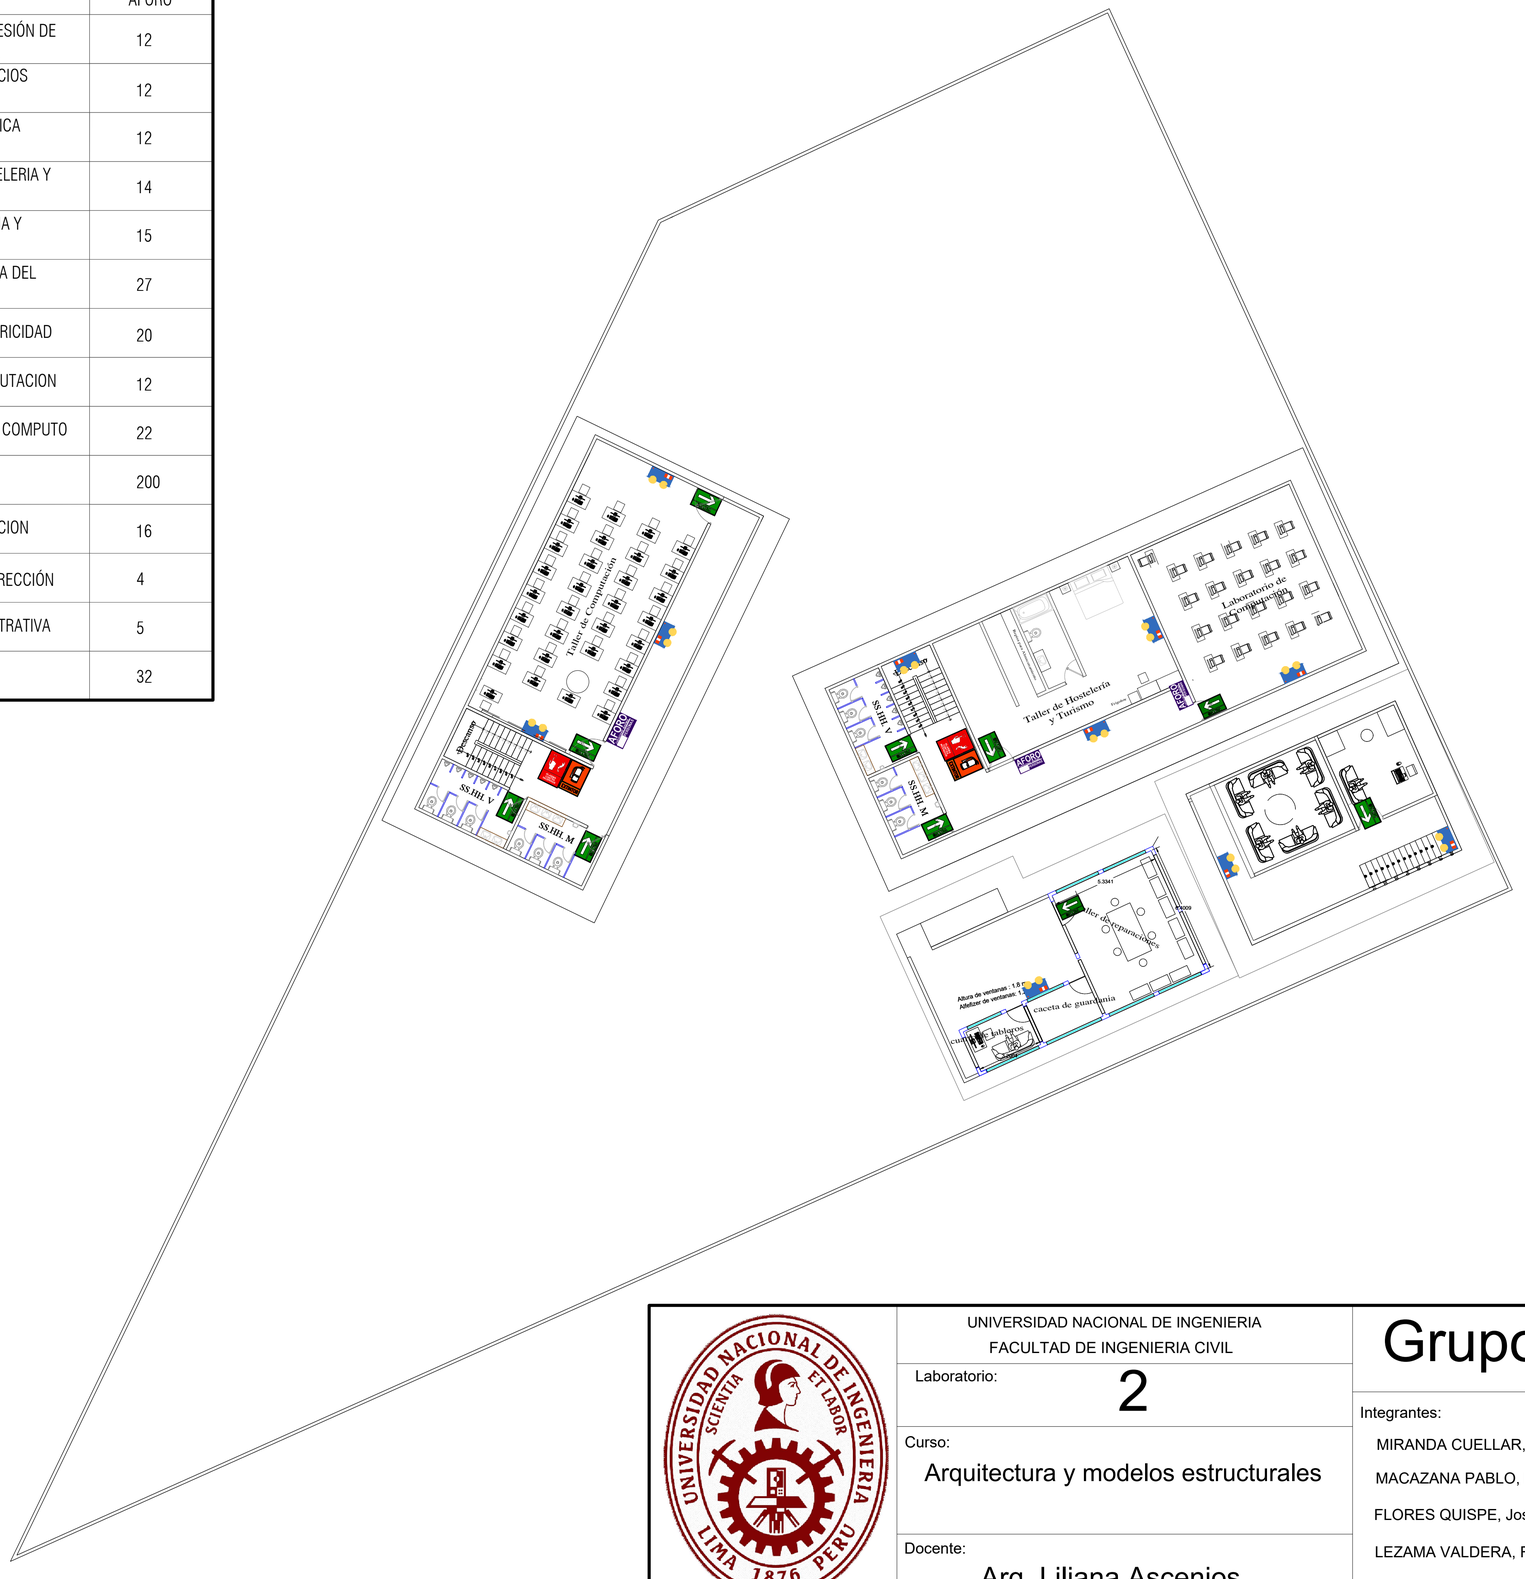

LEYENDA

DESCRIPCION	SIMBOLO
SEÑAL DE SALIDA EN DINTEL DE PUERTA	SALIDA
SEÑAL DE EVACUACION DERECHA E IZQUIERDA	SALIDA / SALIDA
SEÑAL DE ZONA SEGURA EN CASO DE SISMO	S — ZONA SEGURA EN CASOS SISMOS
SEÑAL DE LUCES DE EMERGENCIA	
SEÑAL DE CAPACIDAD DE AFORO	AFORO CAPACIDAD MAXIMA PERSONAS
SEÑAL DE PROHIBIDO EL INGRESO	PROHIBIDO EL INGRESO AREA RESTRINGIDA
SEÑAL DE PULSADOR DE ALARMA	ALARMA CONTRA INCENDIOS
EXTINTOR PORTATIL PQS / CO_2 / H_2O	PQS EXTINTOR
SEÑAL DE ALTO RIESGO	TABLERO PELIGRO ELECTRICO
ZONA SEGURA DE REUNIÓN ANTE EVACUACIÓN	S

UNIVERSIDAD NACIONAL DE INGENIERIA
FACULTAD DE INGENIERIA CIVIL

Laboratorio: 2

Curso: Arquitectura y modelos estructurales

Docente: Arq. Liliana Ascenios

Grupo 4

Integrantes:

MIRANDA CUELLAR, Yaser Feliciano

MACAZANA PABLO, Pier Angel

FLORES QUISPE, Jose Antonio

LEZAMA VALDERA, Renzo Leonardo

CCANA AYUQUE, Joseph Leonardo

Nombre De Proyecto:
Centro de Educacion Tecnico Productivo "ROSA AMERICA"

Tipo de plano: Plano de planta - Arquitectura

FECHA: 13/5/2025

Especialidad: PLANO DE SEÑALIZACIÓN PISO 2

Escala: 1/150

NUMERO DE PLANO: 2